
# PROPOSED GAS MAIN REPLACEMENT
# APPROXIMATELY 1,985' OF 6" PLASTIC - LOW PRESSURE
# 60-157 FULTON STREET, MEDFORD, MA
# W.O. NO. 18746013

| CHA MAIN CONNECTION (MC) IDENTIFICATION LEGEND | |
|---|---|
| PE DESIGN | SOP |
| MC-A | |
| MC-B | |
| MC-C | |
| MC-D | |
| MC-E | |
| MC-F | |
| MC-G | |

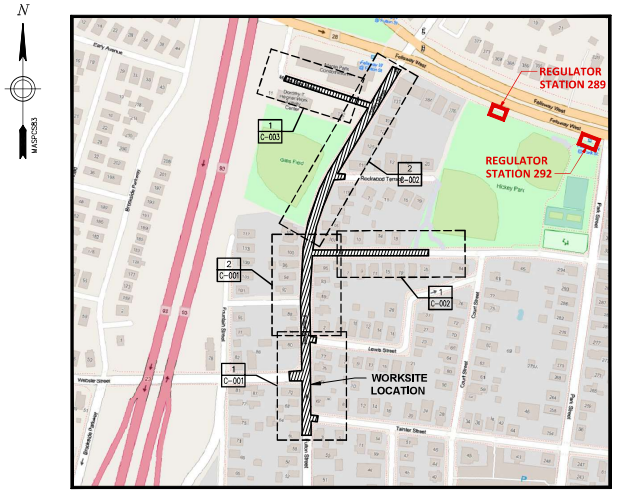


LOCUS
SCALE: 1" = 200'

| INDEX OF SHEETS | | | | |
|---|---|---|---|---|
| | PAGE | DRAWING NO. | SHEET | TITLE |
| | 1 | DPL-MED-093113-1107 | G-001 | COVER SHEET |
| 2 | 2 | DPL-MED-093113-1107 | G-002 | CONSTRUCTION NOTES |
| 2 | 3 | DPL-MED-093113-1107 | G-003 | BILL OF MATERIALS & LEGEND |
| | 4 | DPL-MED-093113-1107 | G-004 | OVERALL SCOPE OF WORK |
| 1 | 5 | DPL-MED-093113-1107 | C-001 | PROPOSED INSTALLATION PLAN |
| 1 | 6 | DPL-MED-093113-1107 | C-002 | PROPOSED INSTALLATION PLAN |
| | 7 | DPL-MED-093113-1107 | C-003 | PROPOSED INSTALLATION PLAN |
| | 8 | DPL-MED-093113-1107 | C-101 | REGULATOR FLOW DIAGRAM |
| | 9 | DPL-MED-093113-1107 | C-102 | REGULATOR FLOW DIAGRAM |
| 2 | 10 | DPL-MED-093113-1107 | C-201 | PROPOSED TIE-IN DETAILS |
| 2 | 11 | DPL-MED-093113-1107 | C-202 | PROPOSED TIE-IN DETAILS |
| | 12 | DPL-MED-093113-1107 | C-301 | NATIONAL GRID STANDARD CONSTRUCTION DETAILS |
| | 13 | DPL-MED-093113-1107 | C-302 | NATIONAL GRID STANDARD CONSTRUCTION DETAILS |
| 1 | 14 | DPL-MED-093113-1107 | C-303 | NATIONAL GRID STANDARD CONSTRUCTION DETAILS |
| | 15 | DPL-MED-093113-1107 | C-304 | NATIONAL GRID STANDARD CONSTRUCTION DETAILS |
| | 16 | DPL-MED-093113-1107 | C-305 | NATIONAL GRID STANDARD CONSTRUCTION DETAILS |

| PIPE TOTALS | | | |
|---|---|---|---|
| DIAMETER (INCHES) | MATERIAL | ABANDONED (FEET) | INSTALLATION (FEET) |
| 4 | CAST IRON | 660 | – |
| 6 | CAST IRON | 1330 | – |
| 6 | COATED STEEL | 5 | – |
| 4 | PLASTIC | 5 | – |
| 6 | PLASTIC | 20 | – |
| 6 | MDPE | – | 1985 |

CHA Project No. 093113-1107

811 DigSafe MA ME NH RI VT

GARY W. PANEBIANCO CIVIL No.52392 REGISTERED PROFESSIONAL ENGINEER
09/28/2026

UNAUTHORIZED ALTERATION OR ADDITION TO THIS DOCUMENT IS A VIOLATION OF APPLICABLE STATE AND/OR LOCAL LAWS

Drawing Copyright © 2026

141 Longwater Drive, Suite 104
Norwell, MA 02061-1620
781-982-5400 . www.chasolutions.com

| NO. | DESCRIPTION | DATE | DR.BY | CK.BY | APP.BY |
|---|---|---|---|---|---|
| 1 | INCORPORATED CLIENT COMMENTS (DATED 09/24/2026) | 09/28/2026 | SL | MLT | GWP |
| 0 | ISSUED FOR CONSTRUCTION | 09/11/2026 | SL | MLT | GWP |

BOSTON GAS COMPANY d/b/a nationalgrid
170 DATA DRIVE
WALTHAM, MA 02451

FINAL

PROPOSED GAS MAIN REPLACEMENT
60-157 FULTON STREET
MEDFORD, MA

COVER SHEET

| DWG SIZE | DESIGNER | ENGINEER | DATE: | ASSET I.D. | W.O. NO.: |
|---|---|---|---|---|---|
| 22"X34" | S. LIAN | M. THOMPSON | 09/11/2026 | DISTRIBUTION | 18746013 |



| DRAWING NO. | SHEET NO. |
|---|---|
| DPL-MED-093113-1107 | G-001 |

File: \\CHA-LIB.COM\PROJ\PROJECTS\MYY\X7\093113.000\09_DESIGN\DRAWINGS\CHA\093113-1107_REV1.DWG
Saved: 9/28/2026 7:54:45 AM Plotted: 9/28/2026 7:55:14 AM Current User: Lian, Solo LastSavedBy: 8637